National
Qualifications
2023 MODIFIED

X835/77/11

Graphic Communication
Supplementary sheets

THURSDAY, 11 MAY
1:15 PM – 3:15 PM

Supplementary sheet 1 for use with question 1 (a) to 1 (d), supplementary sheet 2 for use with question 2 (c), supplementary sheet 3 for use with question 3 (b) and 3 (c), supplementary sheet 4 for use with question 3 (d), supplementary sheet 5 for use with question 4 and supplementary sheet 6 for use with question 6.

©

X8357711



Graphic 1
company logo



Graphic 3
entrance hall poster



Graphic 2
car window sticker




Graphic 4
reusable coffee cup


Supplementary sheet 2 for use with question 2 (c)





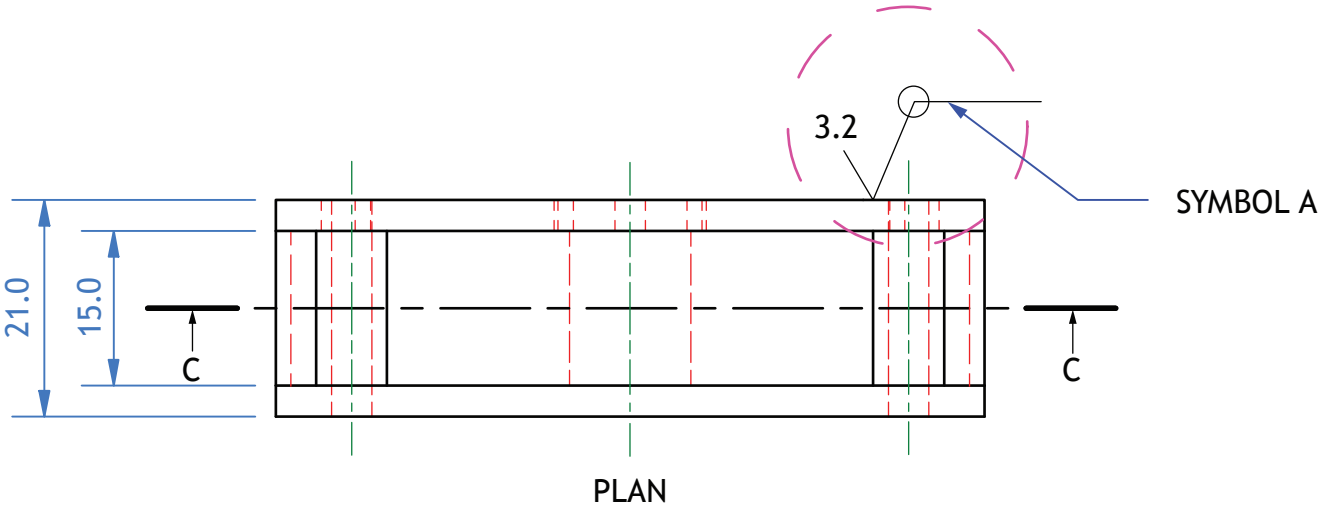


PLAN

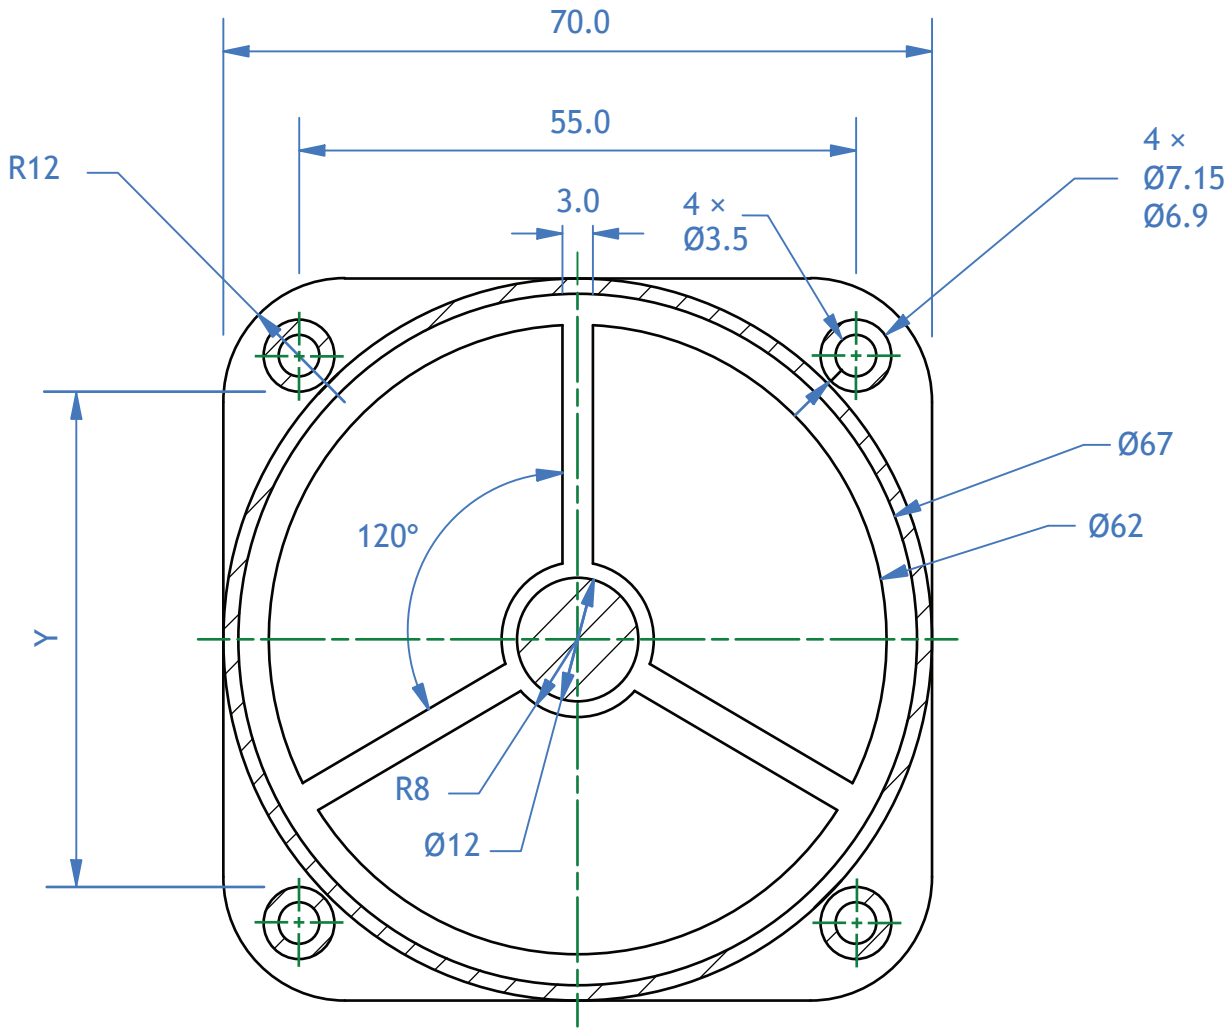

SECTION C-C


SOME CENTRE LINES HAVE BEEN
REMOVED FOR CLARITY

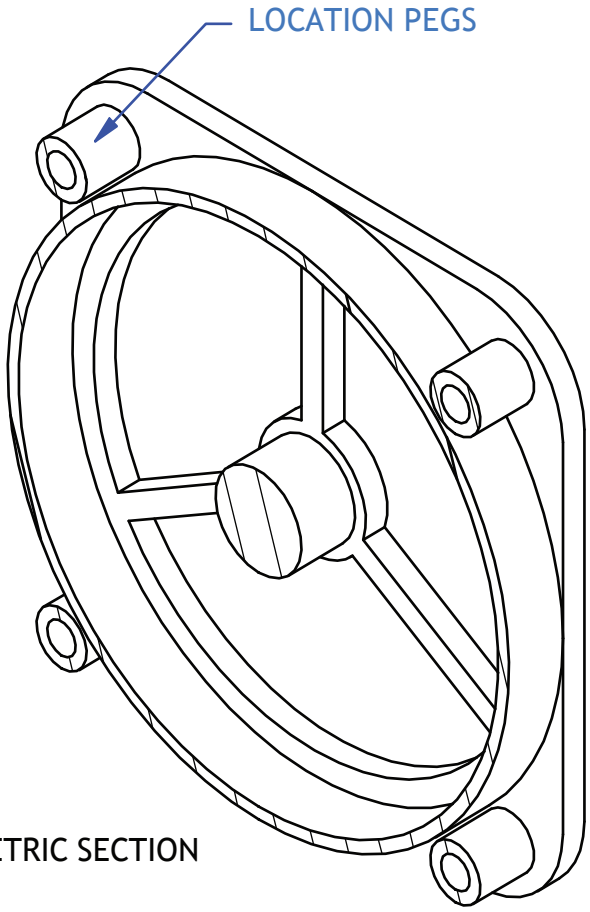

ISOMETRIC SECTION


TITLE FAN: CASING	AUTHOR: A.NON	
DRAWING NUMBER 1		
ALL DIMENSIONS IN MM		SCALE 1:1
TOLERANCE ± 0.01 UNLESS OTHERWISE STATED		DATE: 10/10/22

ISOLATED SINGLE FAN AND CENTRE PIECE

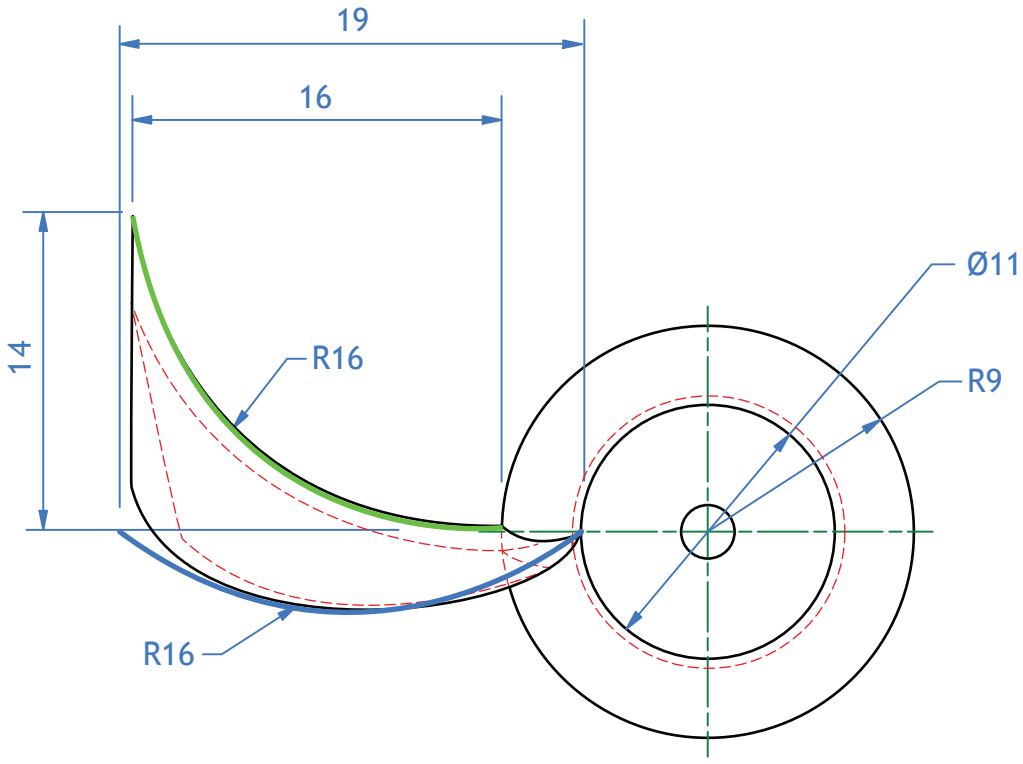


PLAN

THE START POINT OF THE BOTTOM ARC IS HORIZONTALLY ALIGNED WITH THE CENTRE OF THE Ø11 CIRCLE
THE END POINT OF THE BOTTOM ARC IS IN THE POSITION SHOWN ON THE PLAN

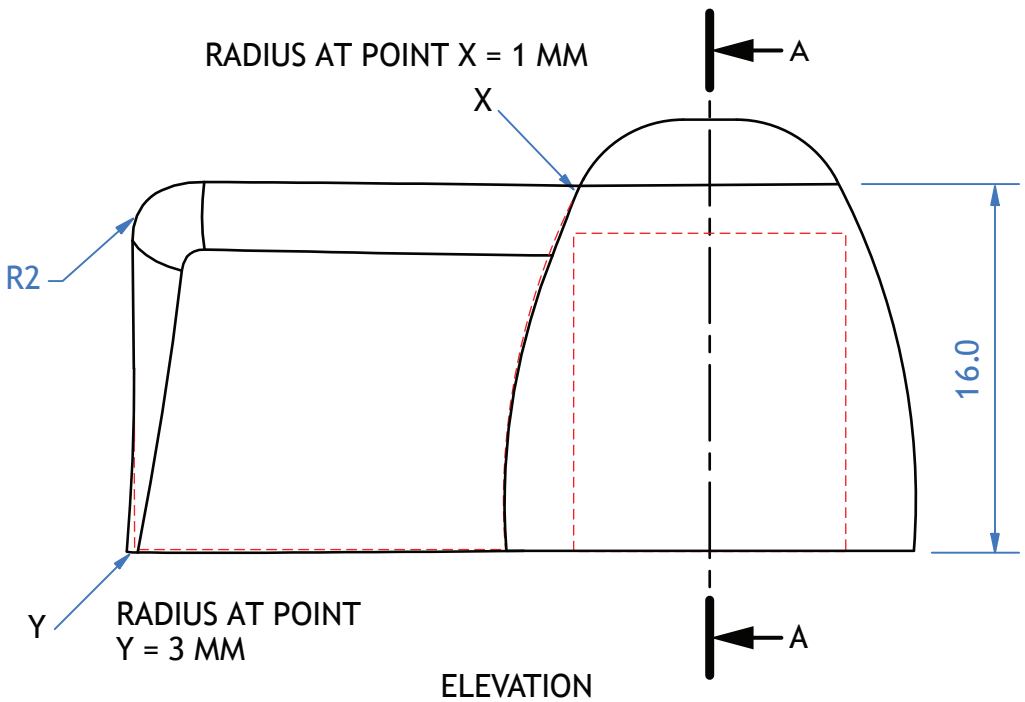



ELEVATION

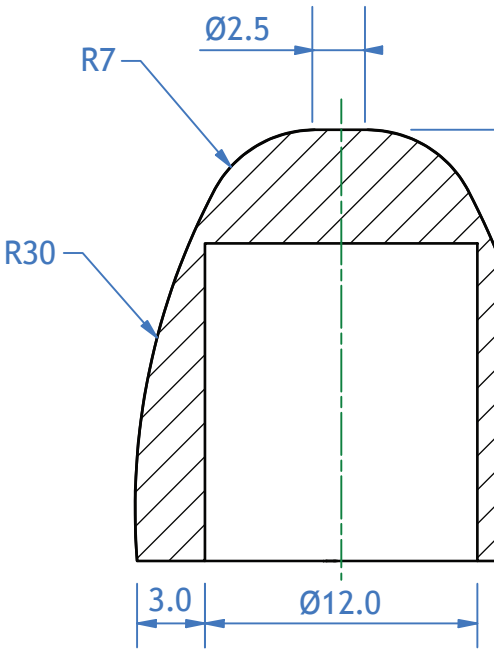


SECTION A-A

THE START AND END POINTS OR THE TOP ARC ARE HORIZONTALLY ALIGNED WITH THE CENTRE OF THE Ø11 CIRCLE.

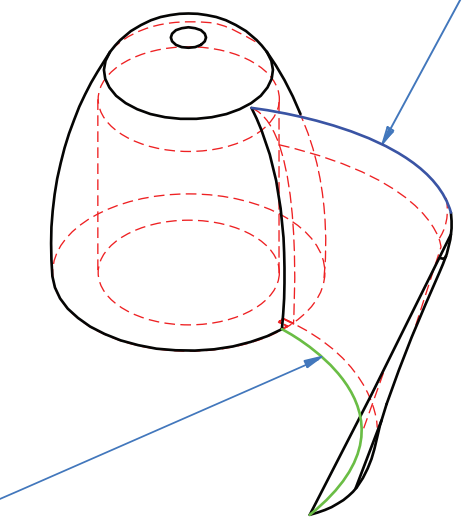


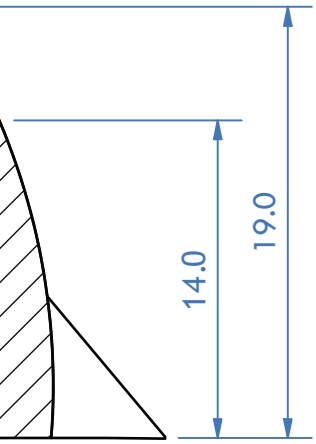

COMPLETED FAN BLADE

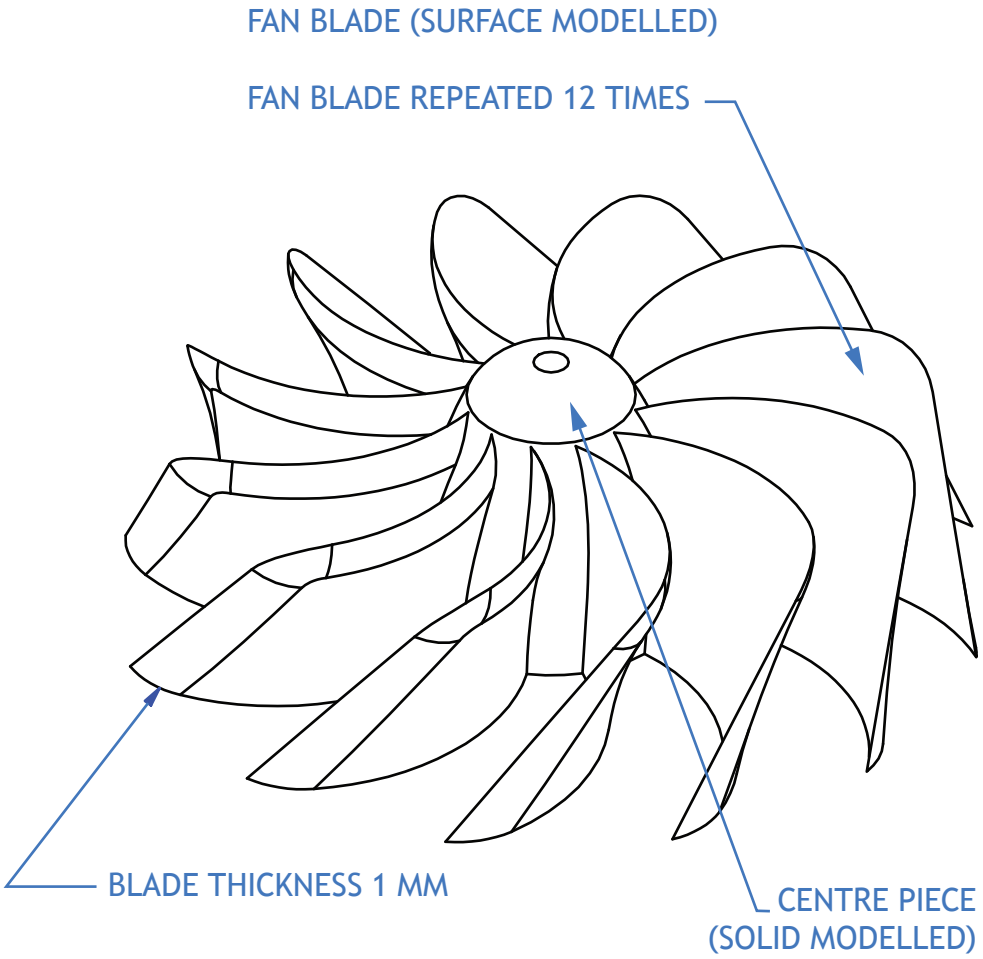

ISOMETRIC

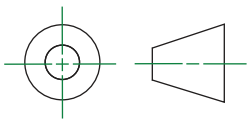TITLE: FAN	AUTHOR: A.NON	
DRAWING NUMBER 2		
ALL DIMENSIONS IN MM		SCALE: 1:1
TOLERANCE ± 0.01 UNLESS OTHERWISE STATED		DATE: 10/10/22


Recommendations
01 / clarity
"this volume makes understanding the complex balance between light space and movement as clear as day."
A.Simpson PhD
02 / research
"a better researched volume on architecture fundamentals you will struggle to find."
A.Jones RIAS
Lorem ipsum dolor sit amet, consectetur adipiscing elit. Integer venenatis faucibu Cras placerat mattis.
E-mail : Lorem ipsu
Website : Lorem ipsu
640509 040147



Vol. 1

Architecture Graphics

June 2022

MK



CONTENT

2022 / SPACE

01 / use of SPACE

Basic skills in the use of space and graphics in architecture, learn skills and tricks from the pros.

02 / use of LIGHT


Basic skills in the use of light to aid decisions of space design especially in new homes and greens spaces.

Use this chapter to explore options in arrange of options in base projects and themes.

TECHNOLOGY

Use of technology in graphics to aid design decisions on projects.


WOODLEA LOCATION PLAN
SCALE 1:1250
CRAIGFLOWER ROAD
BRUNTSFIELD AVENUE
CORSELET ROAD
COMMUNAL PARK AREA
SOLID RUBBER PLAY AREA
NATURE RESERVE
150
150
10
11
12
13
14
15
16
17
18
19
20
21
22
23
24
25
26
27
28
29
30
31
32
33
34
35
36
37
38
39
40
41
42
43
44
45
46
47
48
49
09
08
07
03
02

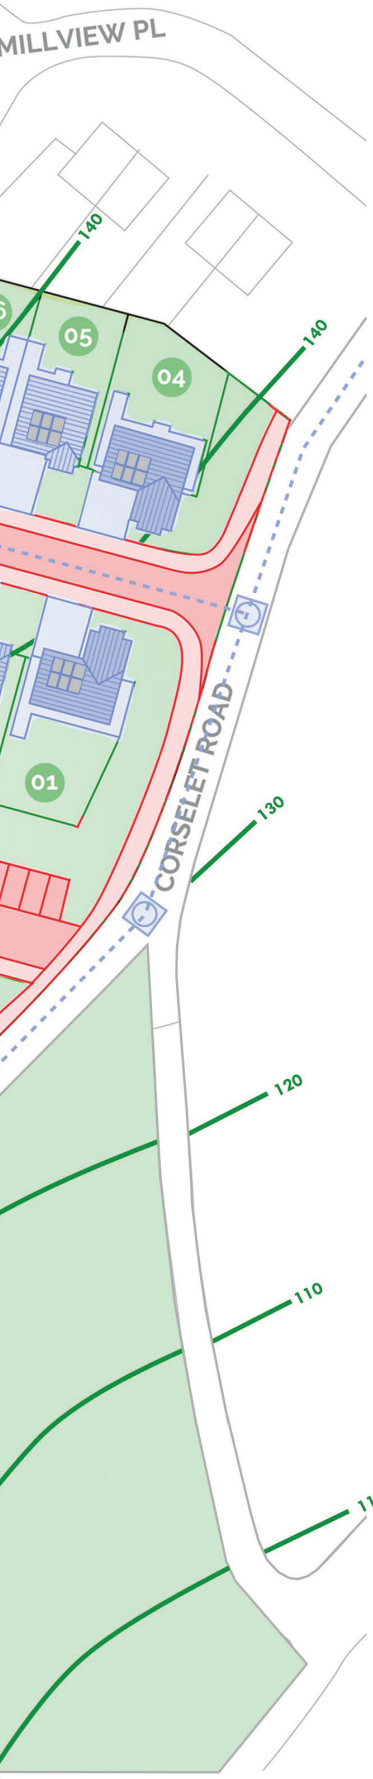

Developer Requirements

Exterior Features and Gardens:

- Turf to all front gardens.
- Rear garden choice of turf or artificial grass.
- Monobloc Driveways
- Paved areas in low cost slab
- Perimeter fencing at rear only
- Solar panelling on all roofs for energy efficiency.

Common Areas:

- Artificial Grass.
- Community Garden
- Fenced around perimeter
- Plants/shrubbery to be included
- Seating made available.
- Children's play area covered in solid rubber with suitable fixtures and fittings for play.

Roads and paving:

- All roads to be laid with compacted tarmac at a depth 50 mm laid on a foundation comprising, 50 mm binder course, 200 mm sub-base and 150 mm sub-grade.
- All paving to be laid using compacted asphalt at a depth of 50 mm.
- Standard concrete kerbs to be laid between tarmac and pavements.

Plot Sizes:

The Oak
3 Bed Detached
96.4m² / 1038ft²

The Hazel
3 Bed Detached
105.6m² / 1137ft²

The Birch
4 Bed Detached
129.4m² / 1393ft²

The Maple
4 Bed Detached
115.1m² / 1240ft²

The Ash
3 Bed Semi-Detached
95.5m² / 1028ft²

The Alder
3 Bed Detached
102.6m² / 1104ft²

The Willow
4 Bed Detached
140.3m² / 1510ft²

The Juniper
4 Bed Detached
134.5m² / 1449ft²

[BLANK PAGE]

DO NOT WRITE ON THIS PAGE

[BLANK PAGE]

DO NOT WRITE ON THIS PAGE

[BLANK PAGE]

DO NOT WRITE ON THIS PAGE

Acknowledgement of copyright

Supplementary sheet 1 kstudija/shutterstock.com

Supplementary sheet 2 korisbo/shutterstock.com

Supplementary sheet 4 TomTomTom CreativeHub/shutterstock.com

Supplementary sheet 6 Woodlea location plan is reproduced by kind permission of Briar Homes.